

Rue du PRE SAINT-GERVAIS de PANTIN

Maîtrise d'ouvrage : Mairie de Pantin
Maîtrise d'œuvre : Segic
Lieu : Rue du PRE SAINT-GERVAIS de PANTIN
Surface : 1 ha
Dates : 2024 - 2025
Montant : 2.270.000 EUR
Missions : Maîtrise d'ouvrage pour les travaux de rénovation et de réaménagement de plusieurs rues, dont la rue du Pré Saint-Gervais et la rue de Pantin.



Contexte:


En tant que chargé de projet, ma mission a été de gérer, avec le maître d'œuvre, la requalification de la rue Pré Saint-Gervais à Pantin. Les principales interventions comprenaient :

- **Mise à sens unique de la rue, avec un contre-sens cyclable.**
- **Élargissement trottoirs côté commerces.**
- **Réorganisation des stationnements**, avec zones de livraison et installation de bornes de recharge rapide.
- **Création de places PMR conformes**
- **Requalification des espaces publics** de façade à façade, incluant 700m² d'espaces verts et la plantation de 8 arbres supplémentaires.
- **Suppression du stationnement** de surface.
- **Réorganisation de la gestion des ordures ménagères.**
- **Installation de dispositifs de ralentissement** de la vitesse des véhicules, nouvel éclairage, dallage granit sur les trottoirs.




Création d'un carrefour en plateau surélevé


Suppression des feux au carrefour remplacés par des stop pour éviter les accélérations

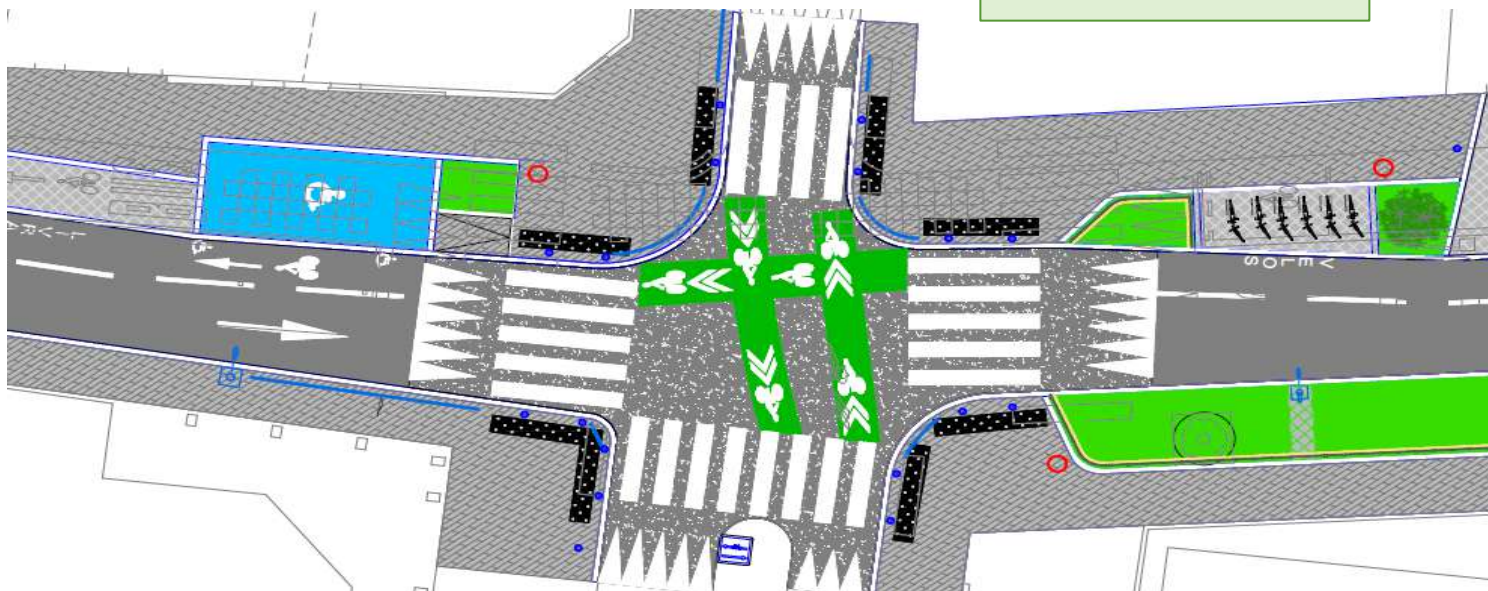


Création traversée piétonne surélevée, dallage granit, désencombrement des trottoirs.

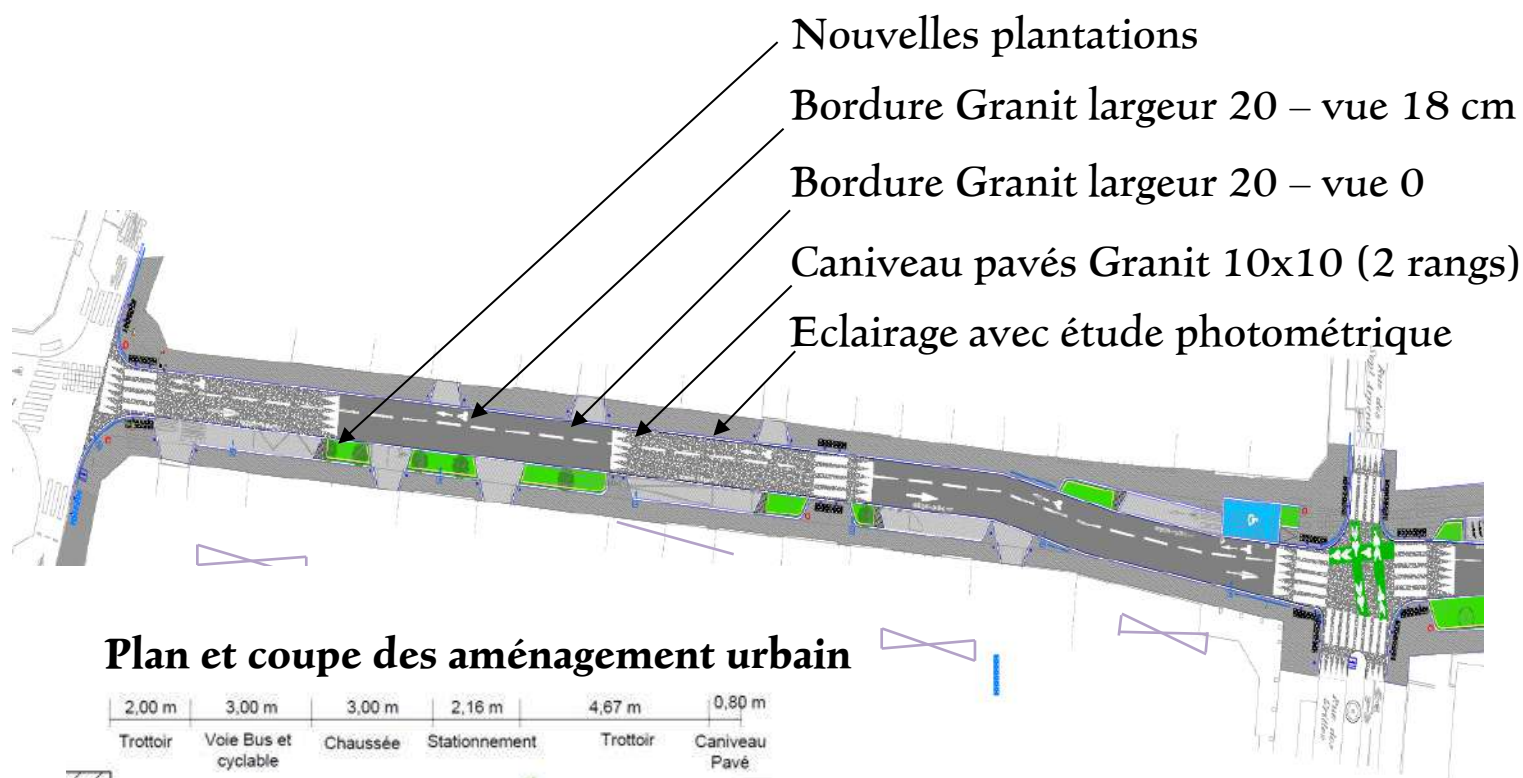

Plan et coupe des aménagement urbain

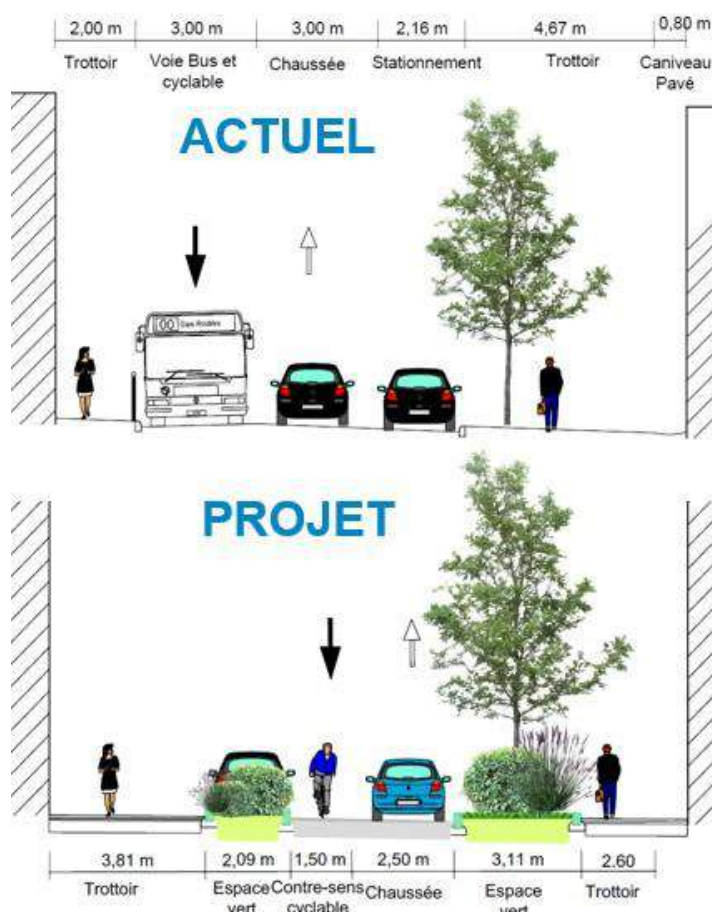

Ma démarche de conception a consisté à réaménager l'espace public en intégrant un nouvel éclairage est bordures chanfreinées des matériaux qualitatifs comme des dalles de granit de différentes dimensions de dalles, avec 2 largeurs et 3 longueurs : 20x40, 20x60, 40x20, 40x40, et 40x60

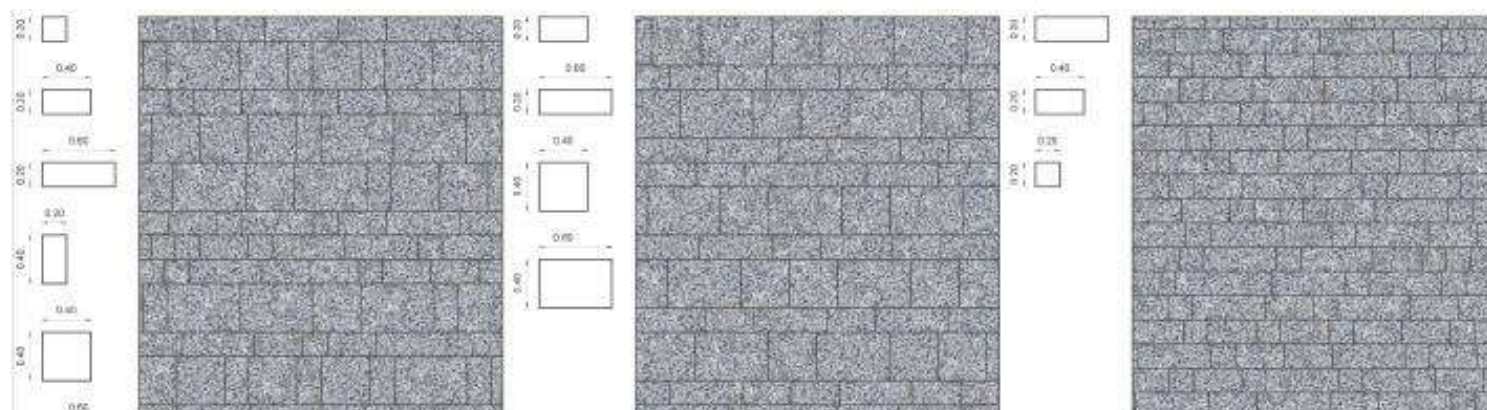

Quartier de l'église St Germain de PANTIN

Maîtrise d'ouvrage : Mairie de Pantin

Lieu : vaste programme de rénovation urbaine est mené dans le quartier de l'Église

Surface : 3 ha

Dates : 2024 - 2025

Montant : 4.460.000 EUR

Missions : Maitrise d'ouvrage pour la rénovation du quartier église de Pantin



Contexte:


Ma mission a consisté à gérer le projet de rénovation urbaine concerne la requalification des espaces publics autour de l'Église de Pantin et de la place du marché en plusieurs étapes :

- **État des lieux et diagnostics :** Analyse des infrastructures, réseaux et usages.
- **Esquisse :** Croquis de l'aménagement des espaces publics.
- **Présentation du projet :** Maquette 3D et animation Lumion pour présenter le projet et impact, incluant l'arrivée du BHSN Tzen3, le marché et le métro.
- **Budget :** Estimation selon l'accord-cadre moyen.
- **Planning :** Calendrier et phasage du chantier.





Maquette numérique
réalisée du quartier

Plans et coupe de l'aménagement autour de l'église

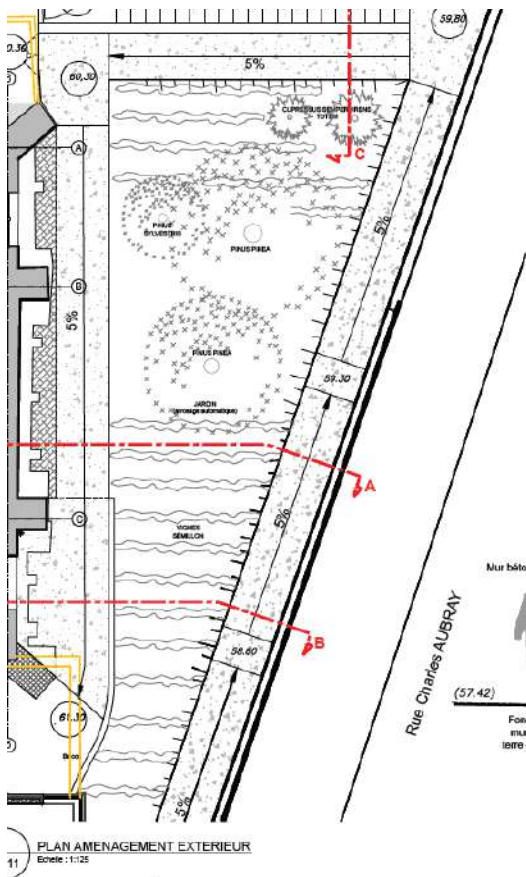

Chargé d'opérations :
Réalisation des esquisses,
plans, coupes, détails
techniques de plantations et
calepinages

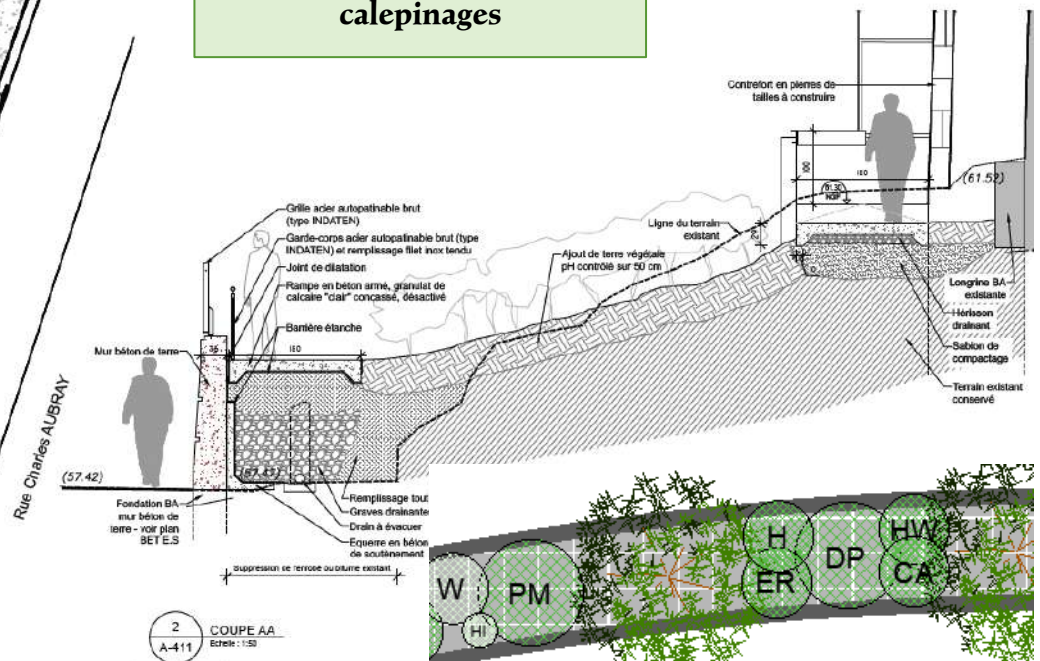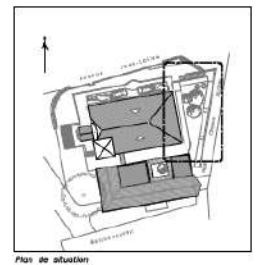

Ma démarche de conception a consisté à réaménager l'espace public pour le connecter harmonieusement au reste de la ville, en tenant compte des nouvelles pratiques de mobilité douce à la sortie du métro, de l'arrivée du BHNS TZEN3, et du réagencement du marché, comme présenté lors des réunions de concertation.

